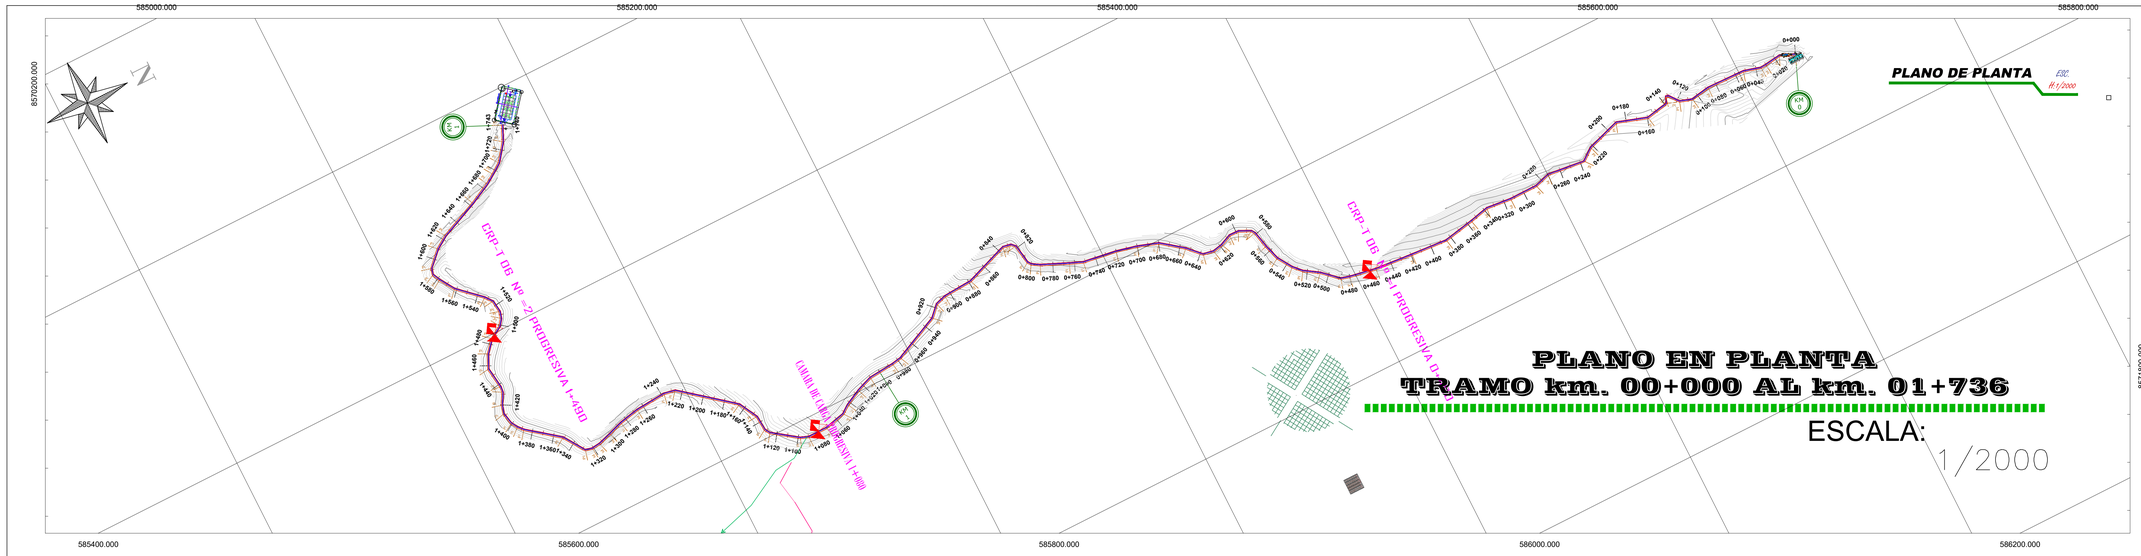

CUADRO DE BMs				
NÚMERO	ELEVACIÓN	NORTE	ESTE	DESCRIPCIÓN
2000	3340.36	8570660.58	585633.48	bm-26
2001	3328.42	8570603.84	585631.89	aux-26
2002	3362.96	8570708.46	585604.02	aux-1.1
2003	3367.83	8570717.86	585592.35	aux-1.2
2004	3365.60	8570803.11	585573.12	aux-1.3
2005	3408.52	8571095.80	585620.93	aux-1.4
2006	3403.63	8571134.92	585650.37	aux-1.5
2007	3322.53	8570477.73	585547.74	AUX-H26.1
2008	3335.04	8570500.32	585528.69	AUX-H26.2
2009	3331.55	8570482.34	585346.36	BM-H28
2010	3330.53	8570484.60	585333.39	AUX-H28
2011	3301.86	8570520.64	584870.58	AUX-HA8
2012	3307.28	8570536.79	585282.49	BM-H29

LEYENDA DEL DIAMETRO DE TUBERÍA		
N°	COLOR	TUBERIA
1		TUBERIA PVC ISO N?? 1452 Dn=32mm
2		TUBERIA PVC ISO N?? 1452 Dn=50mm
3		TUBERIA PVC ISO N?? 1452 Dn=63mm
4		TUBERIA PVC ISO N?? 1452 Dn=75mm
5		TUBERIA PVC ISO N?? 1452 Dn=90mm
6		TUBERIA PVC ISO N?? 1452 Dn=110mm
7		TUBERIA PVC ISO N?? 1452 Dn=160mm
8		TUBERIA PVC ISO N?? 1452 Dn=200mm
9		TUBERIA PVC ISO N?? 1452 Dn=250mm
10		TUB. PVC ISO N?? 1452 POR INSTALAR

ESPECIFICACIONES TECNICAS

El primer relleno compactado que comprende a partirde la cama de apoyo de la tubería hasta 0.30m por encima de la clave del tubo esta al material Tobas Compactado al 95% de la M.D.S. Y el segundo relleno compactado que comprende desprendiendo con fisuras - materiales de 20 a 30 kg de peso - instalado cuidado de no dañar la tubería.

El segundo relleno compactado cuyo comprendido entre el primer relleno hasta el nivel superior del terreno y este de material seleccionado, se hará por capas no mayores de 0.20m y compactado con apisonadores con fisuras manuales.

Para evitar las tuberías y de ellas deslizar fuertemente en sentiendo y evitar alterar las tubería y formarlas a fogal de tubería.

La Prueba Hidraulica se realiza a una presión no mayor de 5 T/cm2 con la presión de la parte mas difícil de una línea hasta fraccion, la fracción de escape se efectuará por la mitad. Y hay algunas circunstancia mas de 24 horas.

LEYENDA CURVA HORIZONTAL

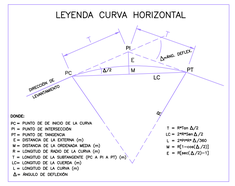

LEYENDA DE CURVA VERTICAL

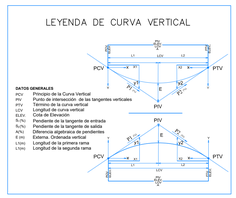

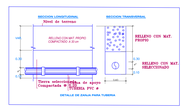

GOBIERNO REGIONAL AYACUCHO

Prider
PROFESIONALES EN INGENIERIA Y CONSTRUCCIÓN
Y DESARROLLO RURAL INTEGRADO

PROYECTO : MEJORAMIENTO Y AMPLIACION DEL SERVICIO DE AGUA PARA RIEGO EN LA ZONA DE ESMERALDA ALTA, DEL DISTRITO DE LURICOCHA Y DISTRITO DE HUANTA - PROVINCIA DE HUANTA - DEPARTAMENTO DE AYACUCHO"

PLANO : **PLANO EN PLANTA Y PERFIL (PROG. 00+000 @ 01+743.19)**

LOCALIDAD : VARIOS	RESIDENTE : ING. GASPAR URBANO MENDEZ		LAMINA N° :
DISTRITO : HUANTA	SUPERVISOR : ING. CESARIO		PYP_01
PROVINCIA : HUANTA			
DEPARTAMENTO AYACUCHO	ESCALA : INDICADA	FECHA : FEBRERO 2025	DIBUJO :
COMISION :HUANCAYOCC			